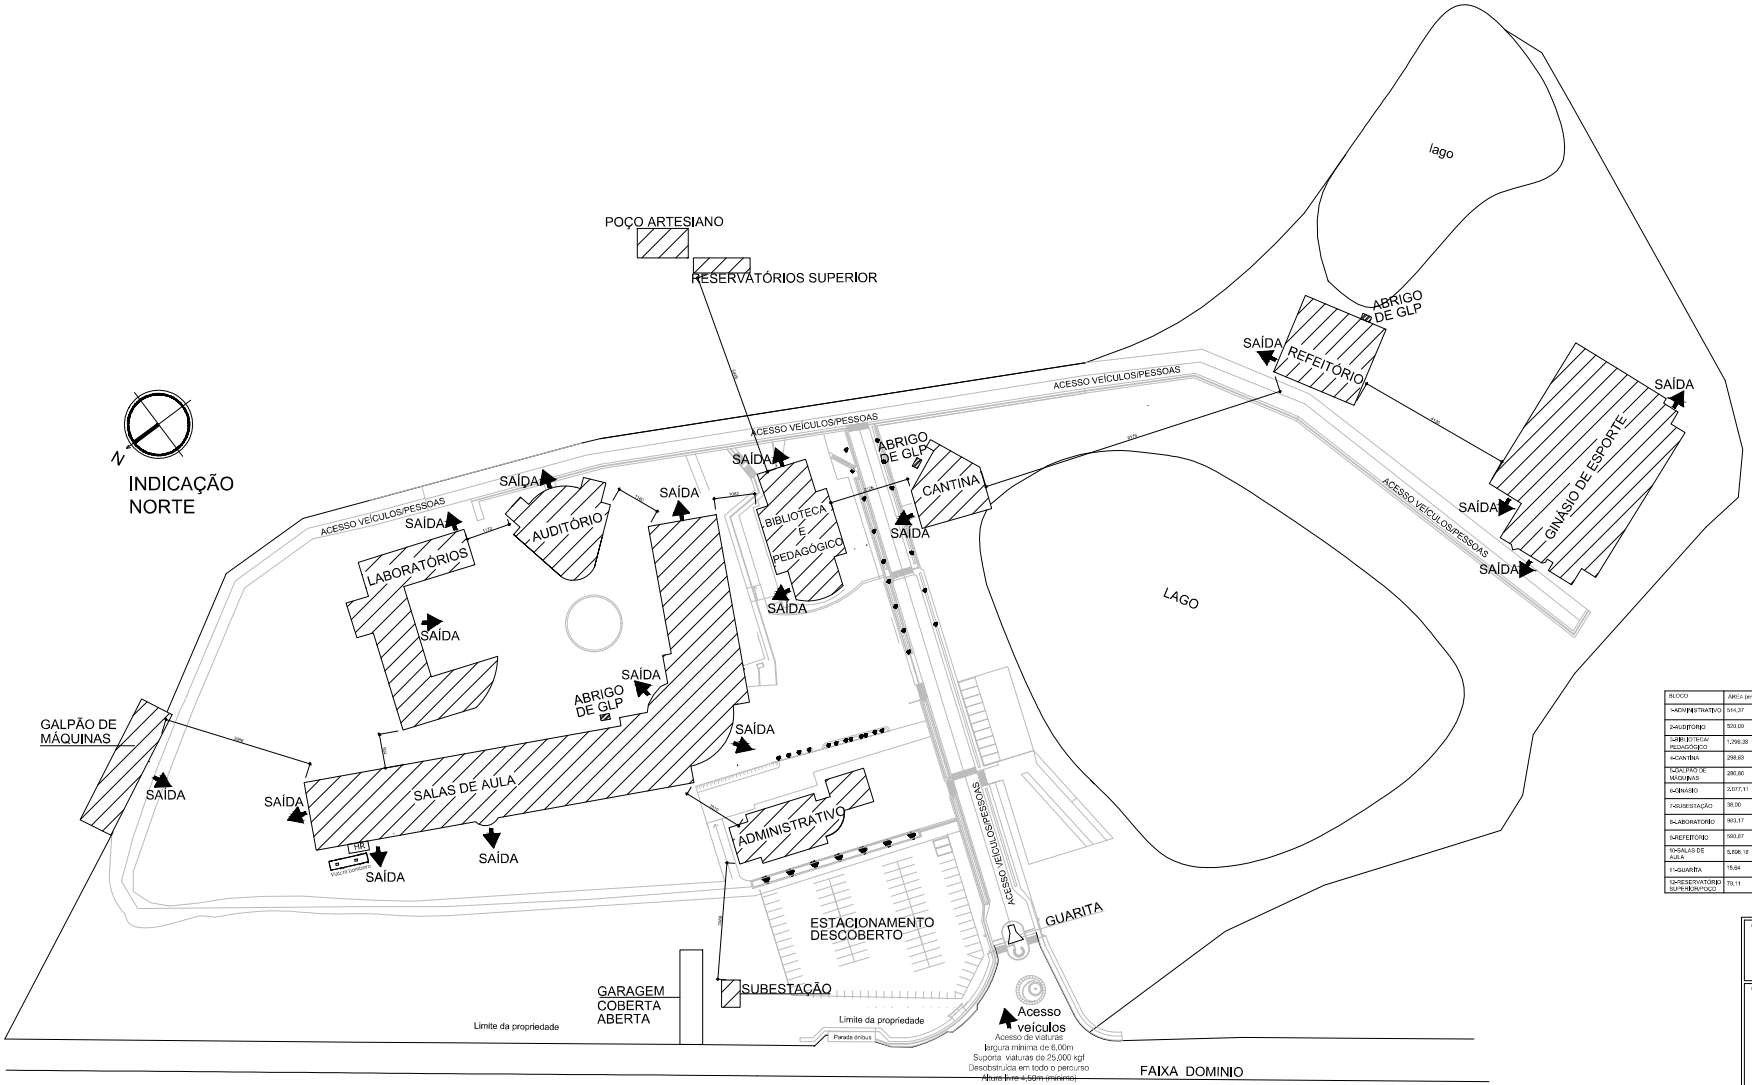

PLANTA DE SITUAÇÃO/LOCAÇÃO
ESC: 1/500

NOTAS Locação de Gás:
O projeto respeita os distanciamentos de segurança:
1,5 m de Locais que possibilitem acúmulo de GLP, como exemplos: fossos, caixas ou ralos de escoamento de água, gordura, ventilação ou esgoto, caixas de rede de luz e telefone, fossa e sumidouro.
6,0 m de Produtos tóxicos, perigosos, inflamáveis ou chama aberta
1,5 m de materiais combustíveis

1. ÁREA TOTAL GLOBAL	12.509,46 m²
1.1. ÁREA BLOCO ADMINISTRATIVO	594,37 m²
1.2. ÁREA BLOCO AUDITÓRIO	520,00 m²
1.3. ÁREA BLOCO BIBLIOTECA/PEDAGÓGICO	1.298,38 m²
1.3.1. ÁREA PAVIMENTO SUPERIOR BIBLIOTECA	630,00 m²
1.3.2. ÁREA PAVIMENTO TÉRREO PEDAGÓGICO	668,38 m²
1.4. ÁREA BLOCO CANTINA	298,83 m²
1.5. ÁREA BLOCO GALPÃO DE MÁQUINAS	280,00 m²
1.6. ÁREA BLOCO GINÁSIO	2.077,11 m²
1.7. ÁREA BLOCO SUBESTAÇÃO	38,00 m²
1.8. ÁREA BLOCO LABORATÓRIOS	863,17 m²
1.8.1. ÁREA PAVIMENTO SUPERIOR LABORATÓRIOS	345,19 m²
1.8.2. ÁREA PAVIMENTO TÉRREO LABORATÓRIOS	959,57 m²
1.9. ÁREA BLOCO REFEITÓRIO	593,87 m²
1.10. ÁREA BLOCO SALAS DE AULA	6.896,18m²
1.10.1. ÁREA PAVIMENTO SUBSOLO	738,32m²
1.10.2. ÁREA PAVIMENTO TÉRREO	2.579,93m²
1.10.3. ÁREA PAVIMENTO SUPERIOR	2.579,93m²
1.11. ÁREA BLOCO GUARITA	15,84m²
1.12. ÁREA BLOCO RESERVATÓRIO SUPERIOR/POÇO	79,11m²

*OBSERVAÇÃO: O Bloco passará por reforma e não será apresentado neste protocolo

BLOCO	ÁREA (m²)	ISOLAÇÃO	OCUPAÇÃO	CARGA DE INCÊNDIO	SITUAÇÃO	HABITE-SE	RISCO
1-ADMINISTRATIVO	594,37	ISOLADO	D1	700 MJ/m²	EXISTENTE	Não possui	II
2-AUDITÓRIO	520,00	ISOLADO	F5	300 MJ/m²	EXISTENTE	Não possui	IV
3-BIBLIOTECA/ PEDAGÓGICO	1.298,38	ISOLADO	F1/D1	969,45 MJ/m²	EXISTENTE	Não possui	III
4-CANTINA	298,83	ISOLADO	F8	300 MJ/m²	RECENTE	Não possui	II
5-GALPÃO DE MÁQUINAS	280,00	ISOLADO	G4	300 MJ/m²	RECENTE	Não possui	II
6-GINÁSIO	2.077,11	ISOLADO	F3	150 MJ/m²	EXISTENTE	Não possui	IV
7-SUBESTAÇÃO	38,00	ISOLADO	K1	300 MJ/m²	EXISTENTE	Não possui	II
8-LABORATÓRIO	863,17	ISOLADO	D4	300 MJ/m²	EXISTENTE	Não possui	III
9-REFEITÓRIO	593,87	ISOLADO	F8	300 MJ/m²	RECENTE	Não possui	II
10-SALAS DE AULA	6.896,18	ISOLADO	E1	300 MJ/m²	EXISTENTE	Não possui	IV
11-GUARITA	15,84	ISOLADO	D1	300 MJ/m²	EXISTENTE	Não possui	II
12-RESERVATÓRIO SUPERIOR/POÇO	79,11	ISOLADO	E1	300 MJ/m²	EXISTENTE	Não possui	II

DESENHADO
* DIREITOS AUTORAIS RESERVADOS - LEI 5988/73
* AO INICIAR A OBRA, COMUNICAR O ENGENHEIRO
* DIVERGÊNCIAS ENTRE COTAS E ESCALAS, PREVALECERÃO AS COTAS
* QUALQUER MODIFICAÇÃO DEVERÁ SER AUTORIZADA PELO RESPONSÁVEL TÉCNICO
* CONSULTAR PROJETO COMPLEMENTARES E VERIFICAR MEDIDAS NA OBRA

LOCAL, DATA E ASSINATURA DO RESPONSÁVEL PELO DESENHO E DO PROPRIETÁRIO

EGS
ENGENHARIA
WWW.EGS.ENG.BR
RUA MARECHAL F. PEIXOTO 525, CENTRO, VIDEIRA-SC
(49) 3533-1670 (49) 99948-3361 (49) 99985-9266

PROJETO PCI IFC - VIDEIRA

ENDEREÇO: RODOVIA SC 135 KM 125, CAMPO EXPERIMENTAL - VIDEIRA SC

ENGENHEIRO: MICHEL TURMINA	INTERESSADO: PROJETO PREVENTIVO CONTRA INCÊNDIO PLANTA DE SITUAÇÃO LOCAÇÃO QUADRO DE ÁREAS QUADRO DE BLOCOS
TÍTULO: INDICADA	PRANCHA: 01
DATA: 01/2024	IN 01/15
ÁREA: 12.509,46 m²	
CREA: nº 9089951-0	

ASSINATURA DO RESPONSÁVEL TÉCNICO: MICHEL TURMINA CREA-SC 089951-0 CPF: 062.310.949-28 — MICHEL TURMINA:06231094928 Assinado de forma digital por MICHEL TURMINA:06231094928 Dados: 2024.01.08 14:58:15 -03'00'

ASSINATURA DO PROPRIETÁRIO: Instituto Federal Catarinense (IFC)
CNPJ: 10.673.179/0001-31

CORPO DE BOMBEIROS MILITAR DE SANTA CATARINA
02º BATALHÃO DE BOMBEIRO MILITAR - SERVIÇO DE SEGURANÇA CONTRA INCÊNDIO - VIDEIRA-SC
PROJETO PREVENTIVO CONTRA INCÊNDIO
Decreto Nº 2.718 de 06 de Novembro de 2013 - Lei Complementar Nº 426 de 05 de Outubro de 2009 